



220kV 户外AIS 典型间隔断面图

220kV 户外AIS 典型间隔断面图 (规程表7-2, mm)
A1=1800 A2=2000 B1=2550 B2=1900 C=4300 D=3800

- 断面标高以当地±0.000 为基础; 尺寸单位为m, 电气净距单位为mm。
- 无遮栏导体对地C≥4.30m; 本图系指主要带电端子标高5.00m。
- 相同断系指4.00m, 必须大于A2=2.00m 与规程检修要求。
- 设备高度与占位为净距几何数据, 正式工程及理由厂家外数据, 端子高度和基础数据。
- 规程设计数据: 海拔≤1000m, 污秽≤3 级; 海拔≤1000m 或污秽更严处应重新校核绝缘与净距。
- 净距表采用规程表7-2 表7-2 表220J 内; 正式工程或施工参考DL/T 5352-2018 正文复核。



线路间隔断面 A-A

三相导线横断面示意图

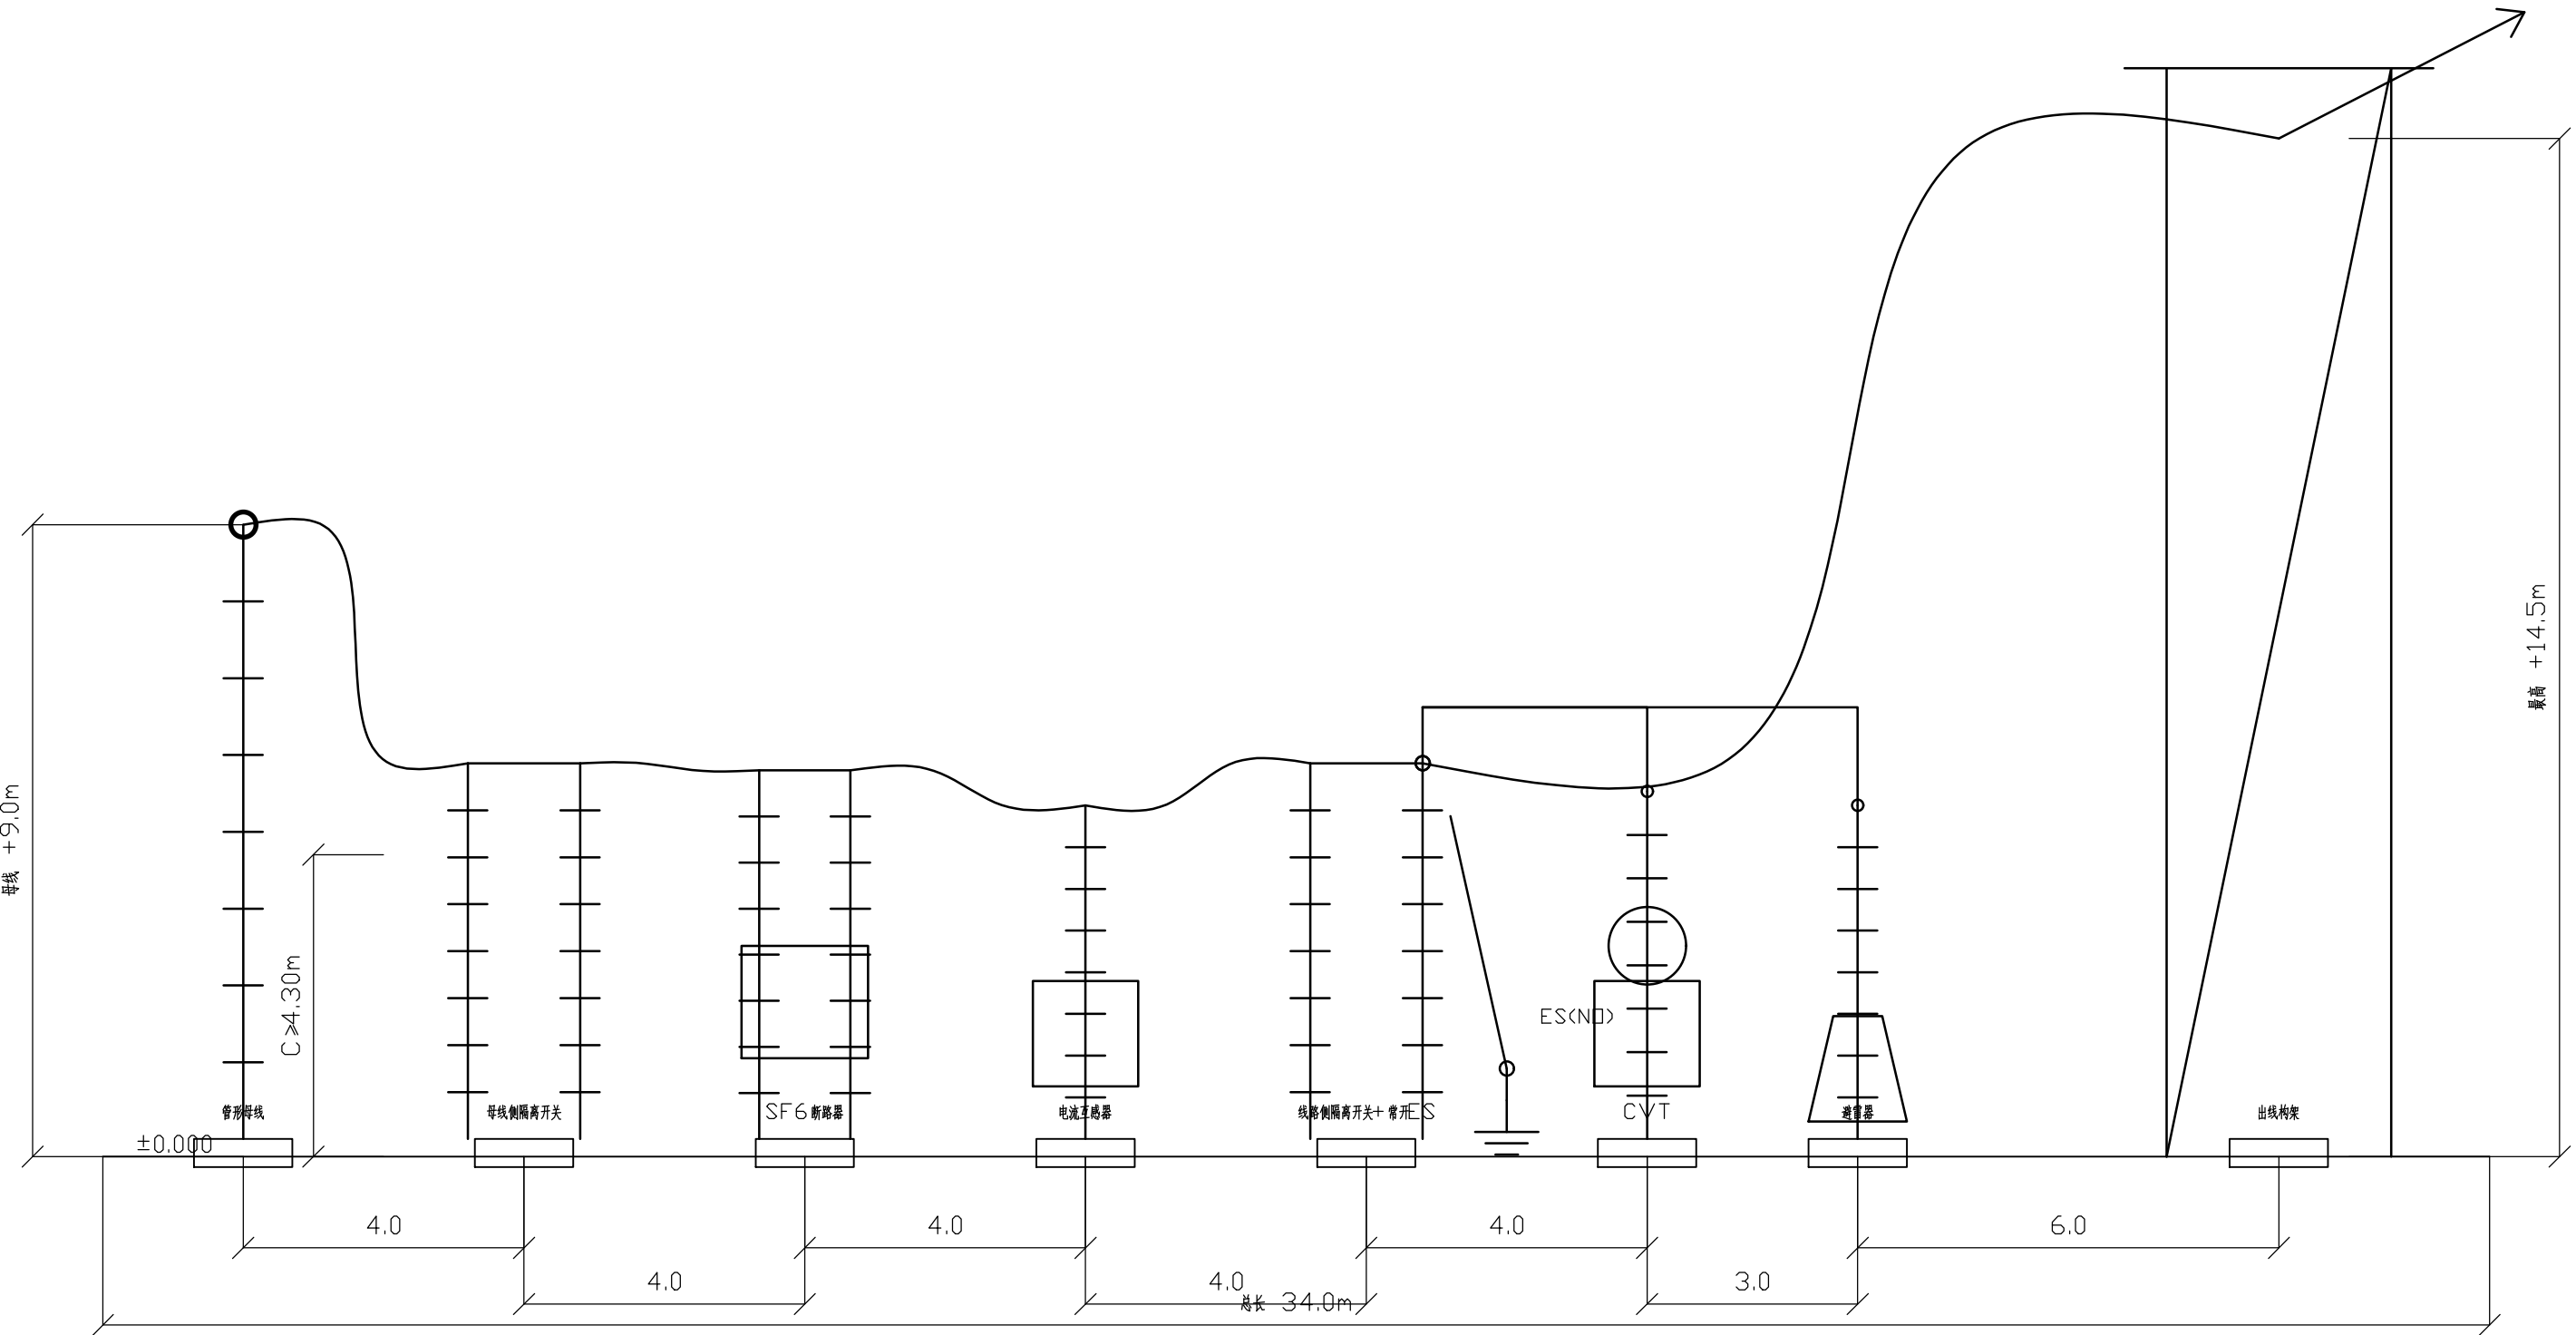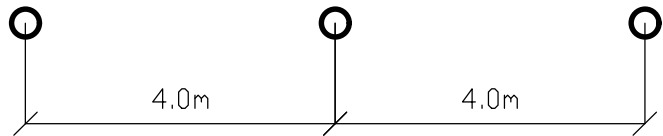

主变间隔断面 B-B

三相导线横断面示意图

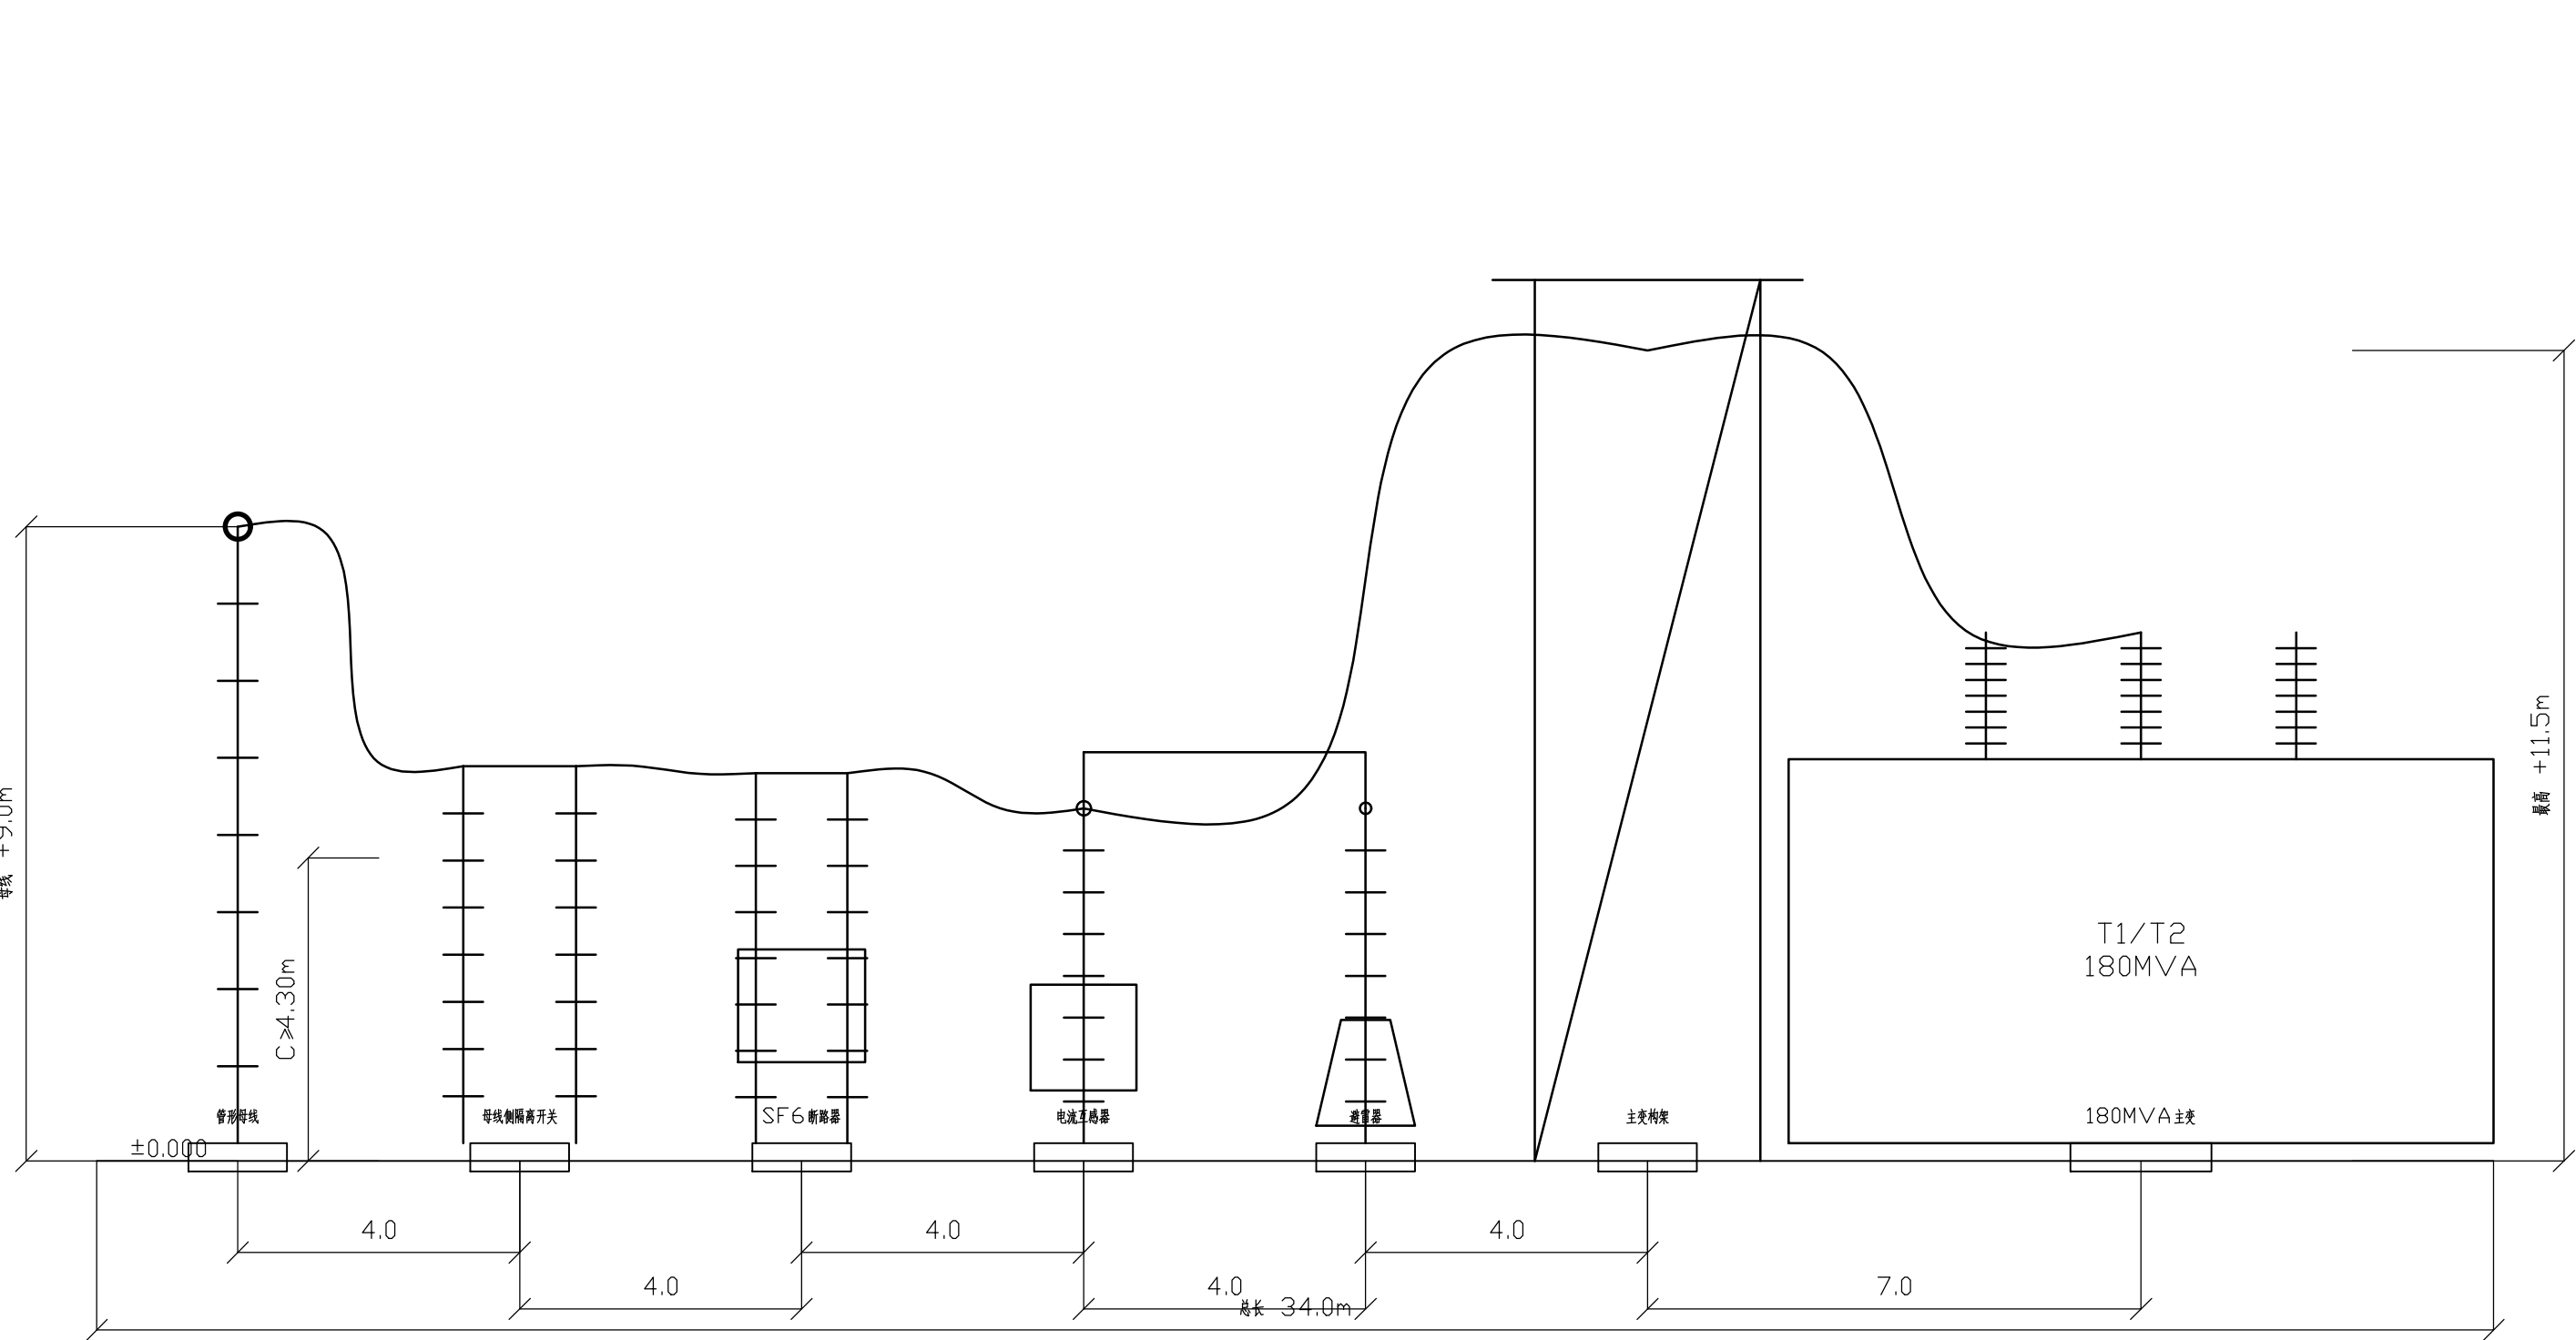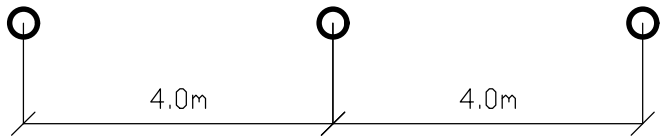

220kV 户外AIS 典型间隔断面图

图号 SEC-220-01

第1 页 共1 页

220kV 新能源汇集发电所电气一次部分

设计

设计

设计

比例 1:100