


220kV 新能源汇集变电所电气主接线简图

220/35/10kV-次系统 结构化数据驱动工程底图

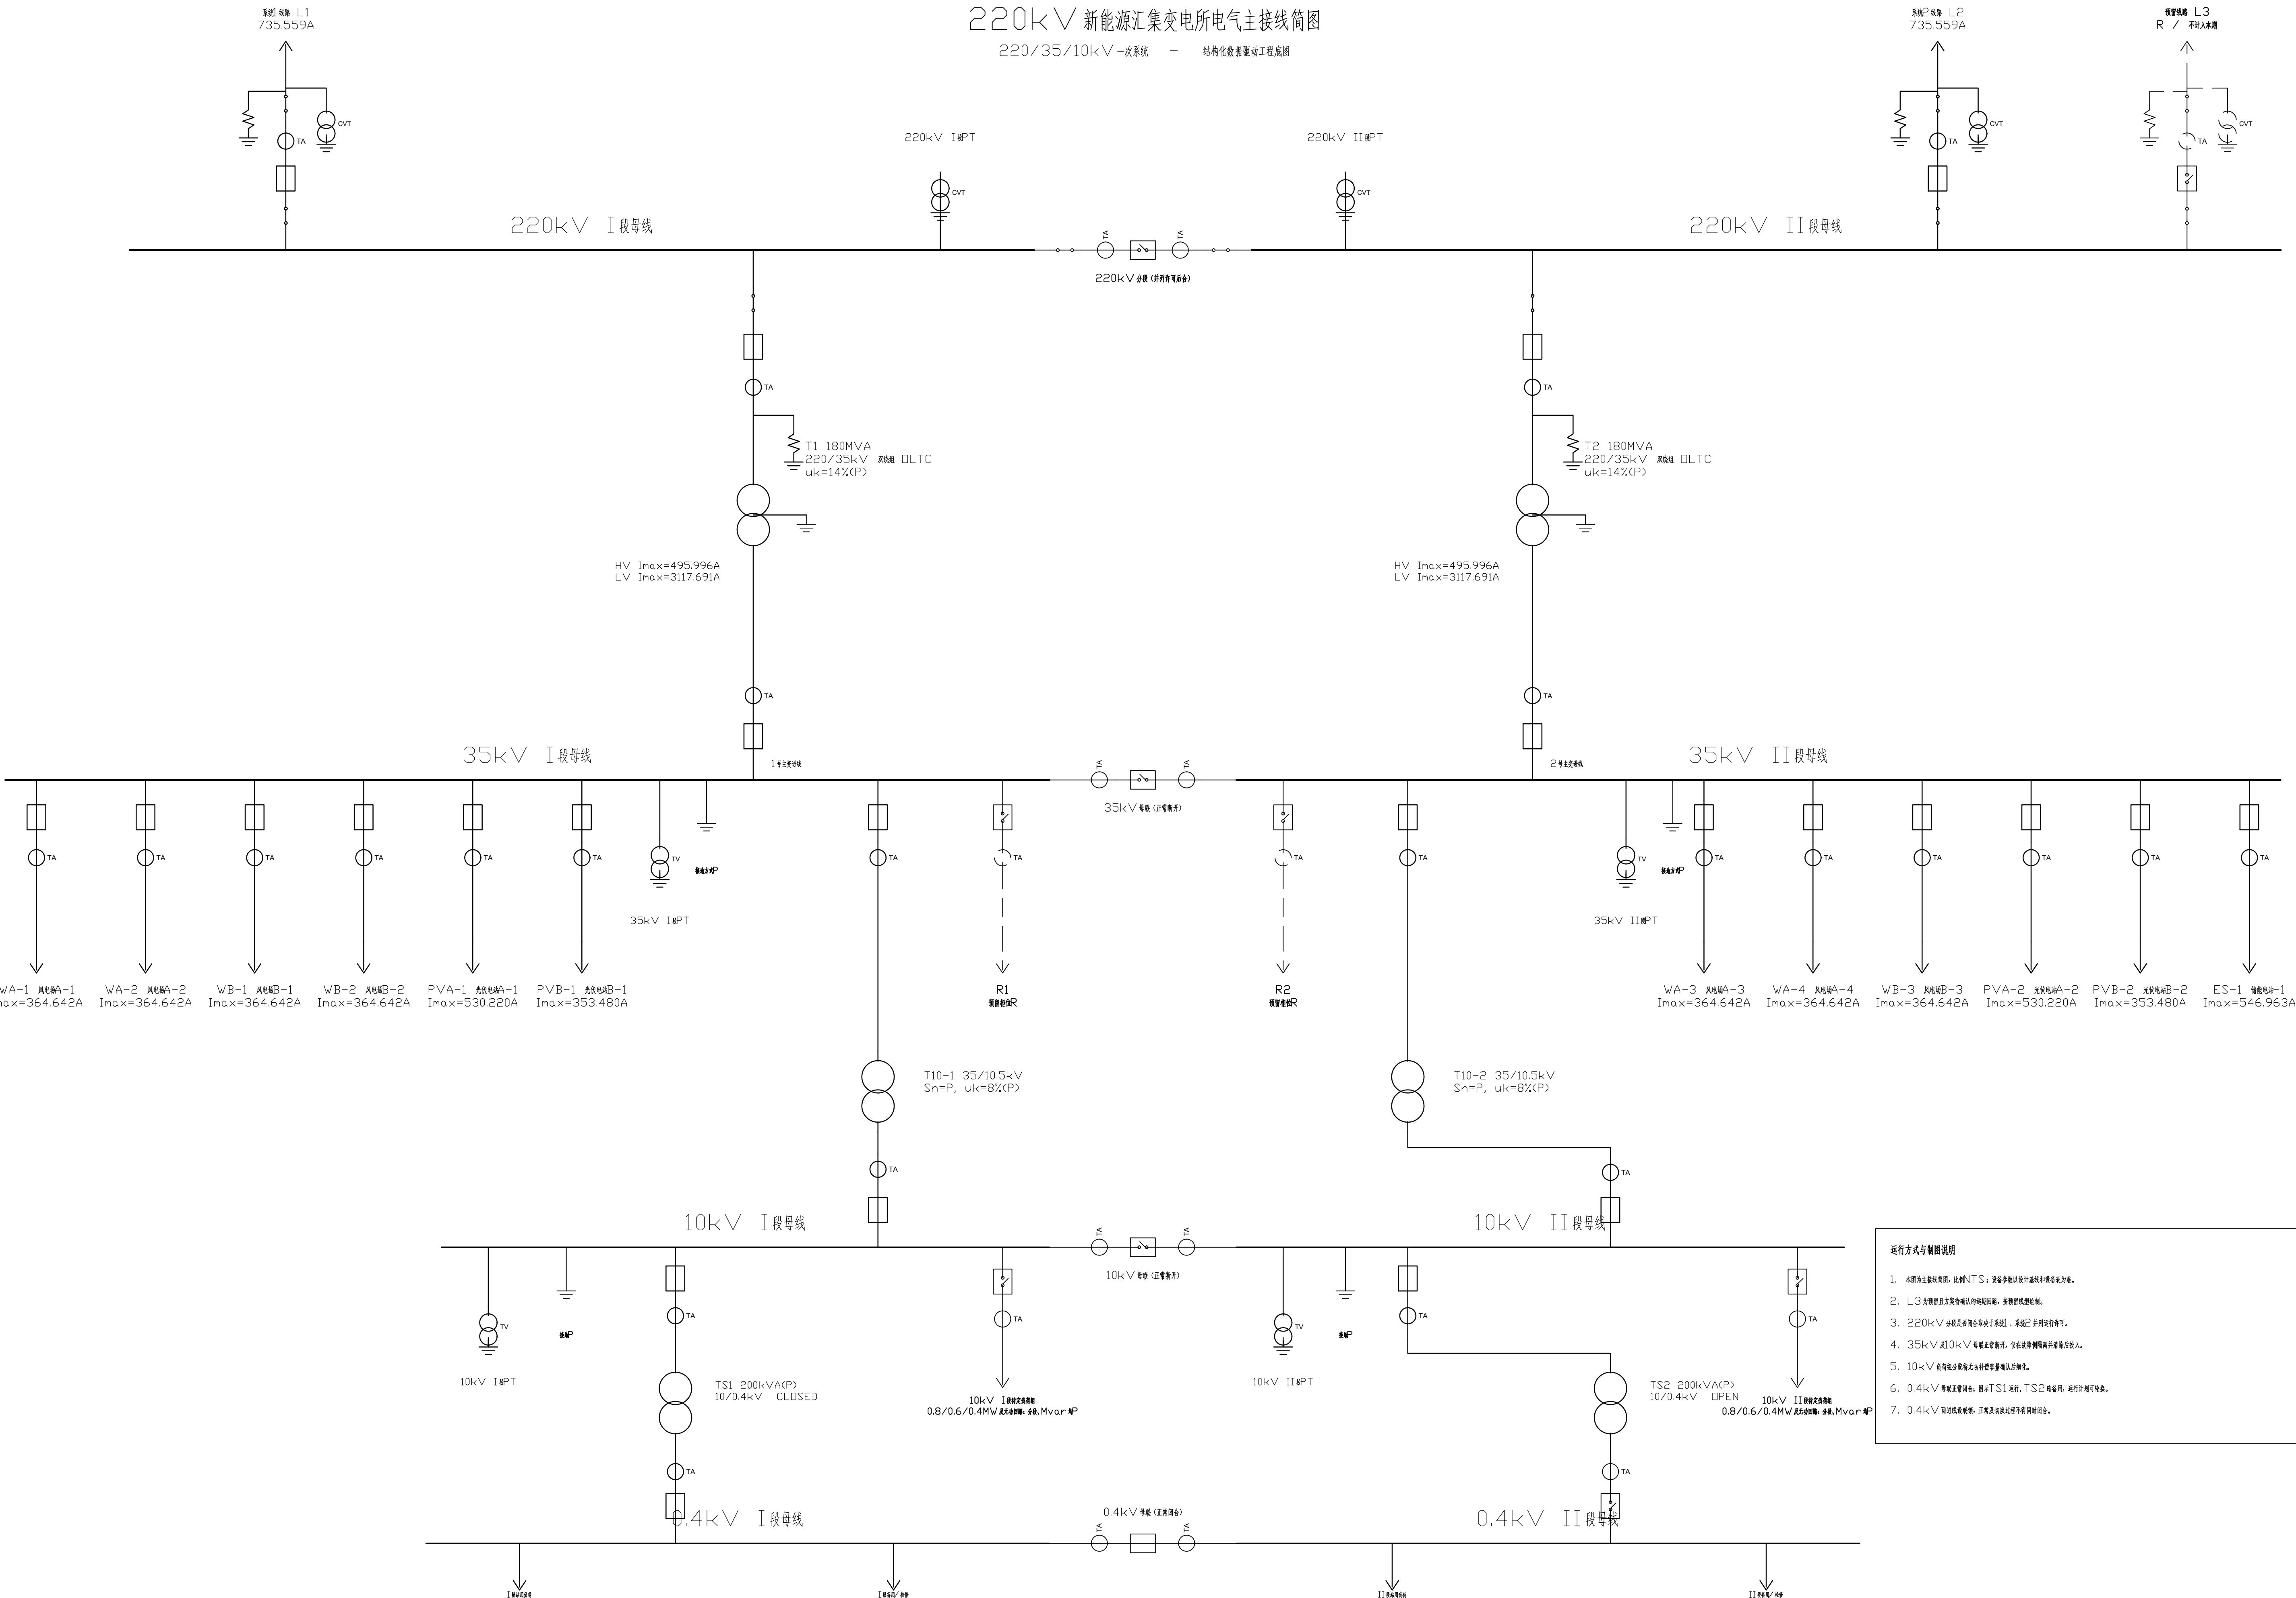

运行方式与制图说明

- 本图为主接线简图，比例1:1；设备参数以设计基础和设备铭牌为准。
- L3为预留压注变接确认的线路，按预留线路绘制。
- 220kV分接变接确认的线路，系统2并列运行。
- 35kV10kV等接正常断，仅在故障时隔离并确认后投入。
- 10kV线路按分配给无设计变接确认后投入。
- 0.4kV等接正常断，按TS1运行，TS2备用，运行计划可转换。
- 0.4kV两母线及线路，正常及故障时不得同时运行。

图例: QF—断路器 QS—隔离开关 TA—电流互感器 TV/CVT—电压互感器 MDA—避雷器 P—暂态 R—预留 NQ—正常断

制图说明: 精确型号、CT/PT变比、T10容量、10kV无功Mvar、海拔及污秽等级均未标注。220kV分接变接确认: 35/10kV等接正常断; 0.4kV按单台所用变运行、等接网合表述。

公开包库工程底图: 课程提交是否允许直接使用CAD输出须由指导教师确认。

220kV 新能源汇集变电所电气主接线简图

图号 SLD-01

第1张 共1张

电气一次部分初步设计

课程设计

设计:

校核:

比例 NTS