


## 220kV I 段 L1 线路间隔断面详图

| L1 线路间隔额定参数表 |                                                                        |
|--------------|------------------------------------------------------------------------|
| 系统/电压        | Un=220kV; Un=252kV; L1WV=950kV                                         |
| QF 额定电流      | 252kV: 3150A; 50kA(3s); 额定 25kA                                        |
| QS 额定电流      | 252kV: 3150A; 50kA(3s); 额定 25kA                                        |
| TA/CVT       | TA=1000/1A; CVT=220/√3kV / 100/√3V, 额定短路 100/√3V 和 0.3%; 二次负荷/准确限值系数表见 |
| MDA          | YH10W-204/532; Uc=159kV; In=10kA                                       |
| 绝缘/避雷        | 0100/90 额定绝缘电压: 额定 4.0m; A1/A2/C 见图                                    |

## 设计说明与边界

1. 本期共 1 个中间国家设计项目，设备外购、基础和端子柜材料由供货厂家直接量。
2. 线路图 QS 和管架 ES，并和 QS、QS 装置名称/电气图名称；按修改线路图提供图例。
3. 地下接地网与设备/构筑物接地连接示意图：接地电压、接地电压和电压电流需专项计算。
4. MPA 用于指导电缆电压降测试；本期不代表全系统管理/建设国家主要保护系统完成。

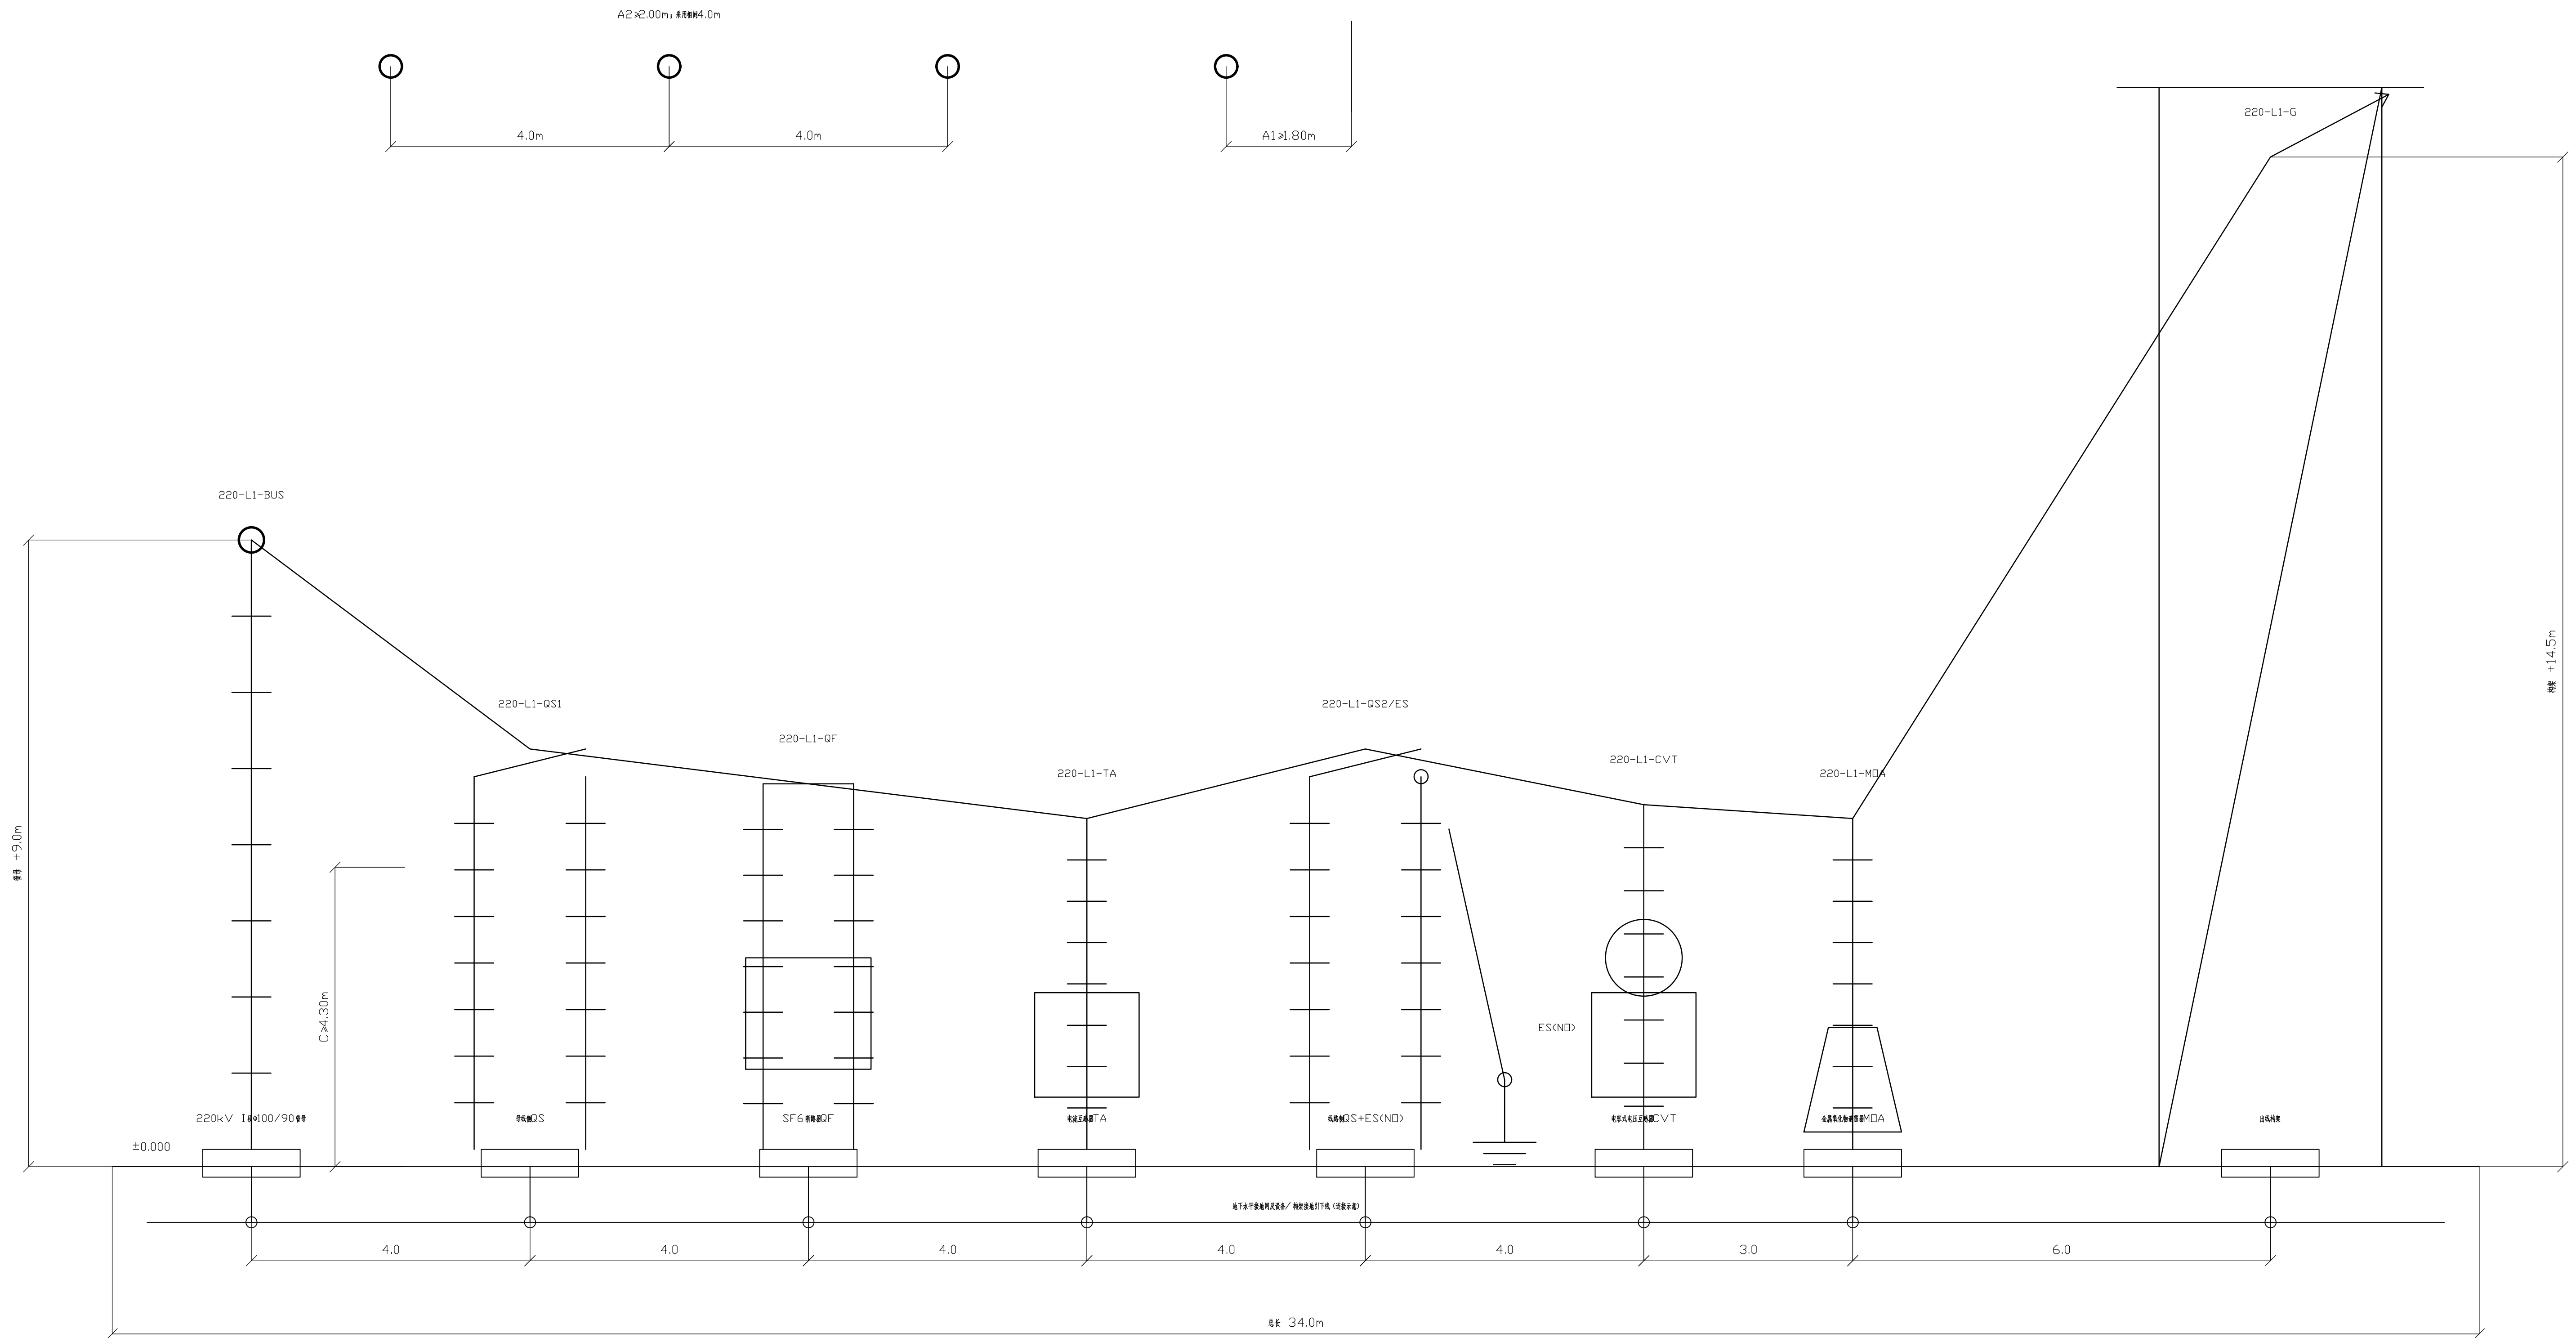

|                      |     |                  |         |
|----------------------|-----|------------------|---------|
| 220kV I 段_1 线路间隔断面详图 |     | 图号 SEC-220-L1-01 |         |
|                      |     | 第1张 共1张          |         |
| 220kV 新能源汇集变电站电气一次部分 |     |                  |         |
| 项目设计                 | 设计: | 审核:              | 比例 1:50 |