


220kV 户外AIS 配电装置平面布置图

220kV 户外最小净距 (硬母线7~2.0mm)
A1=1800 A2=2000 B1=2550 B2=1900 C=4300 D=3800

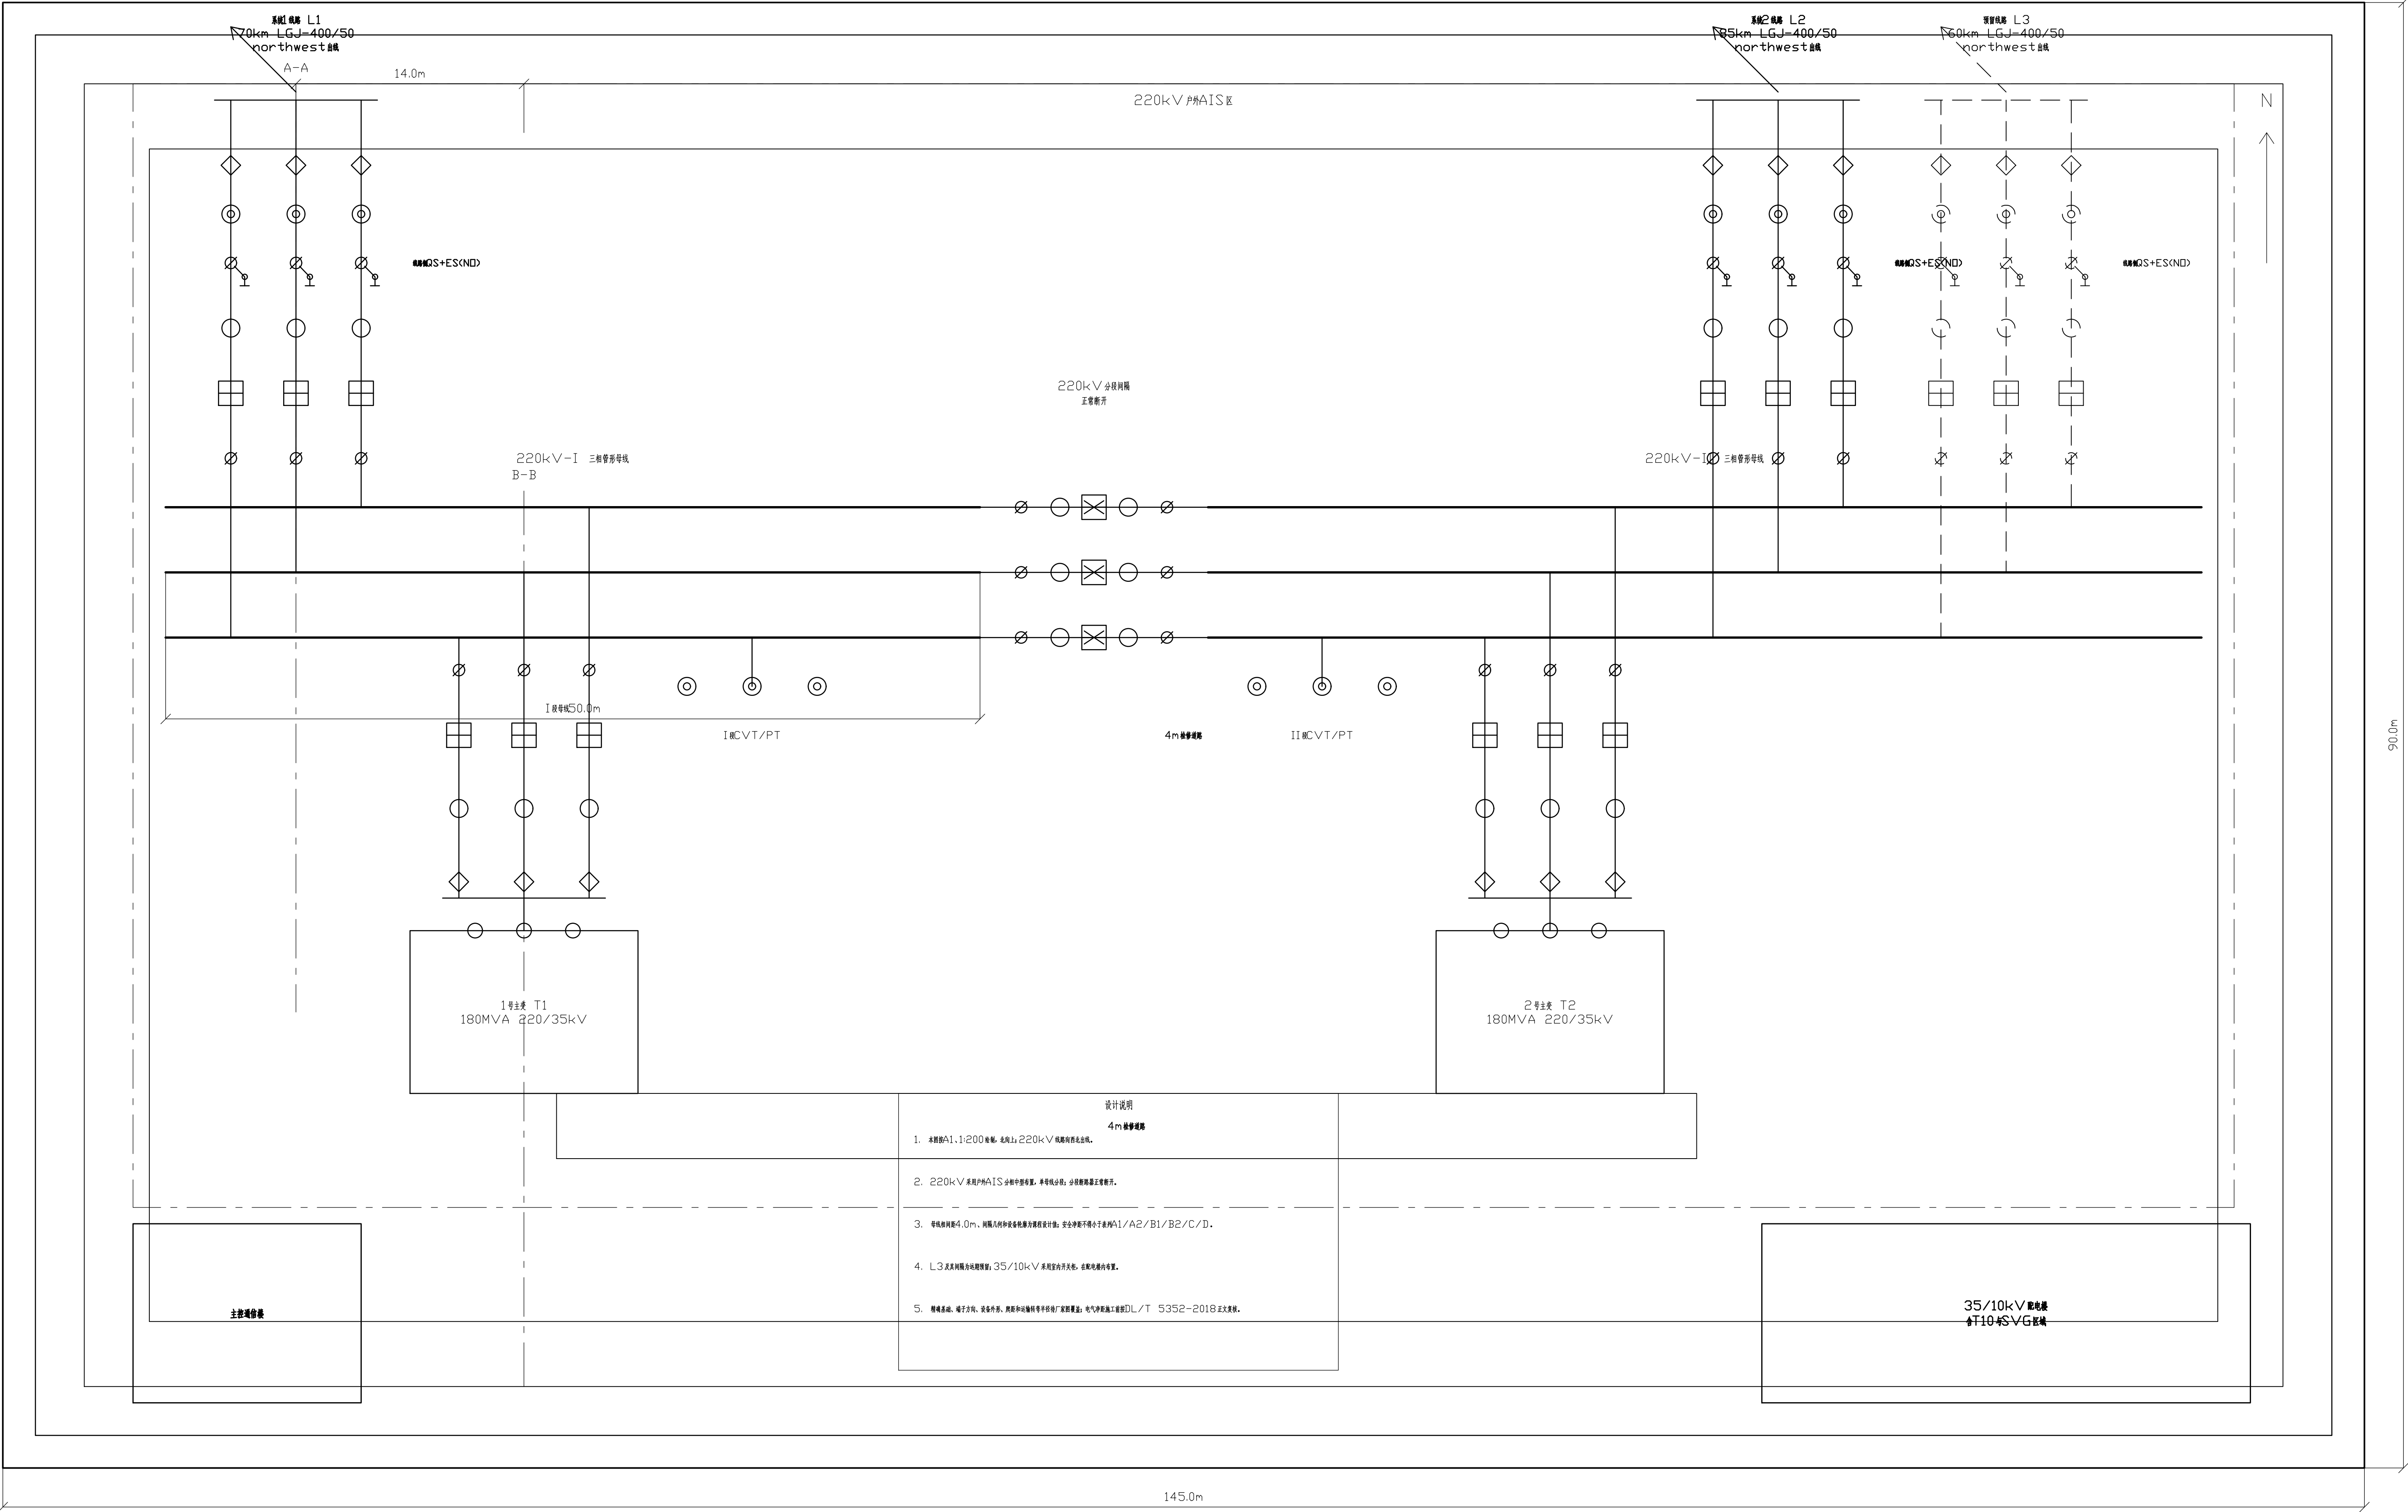

- 设计说明
4m 检修道路
- 本图按A1、1:2000 绘制, 本图在 220kV 线路同侧布置。
 - 220kV 采用户外AIS 分相布置, 单母线分段, 分段断路器正常断开。
 - 导线截面4.0m, 间隔尺寸按设备布置图设计, 安全净距不小于A1/A2/B1/B2/C/D。
 - L3 及其间隔为运维通道, 35/10kV 采用室内开关柜, 在柜体上方布置。
 - 检修通道、端子走向、设备名称、间隔和间隔尺寸等应符合《变电站设计》、《电气设备安装工程》DL/T 5352-2018 规定。

220kV 户外AIS 配电装置平面布置图			图号 LAY-220-01	
			第1页 共1页	
220kV 新疆准汇集发电所电气一次部分				
设计	校核	审核	批准	比例 1:200